


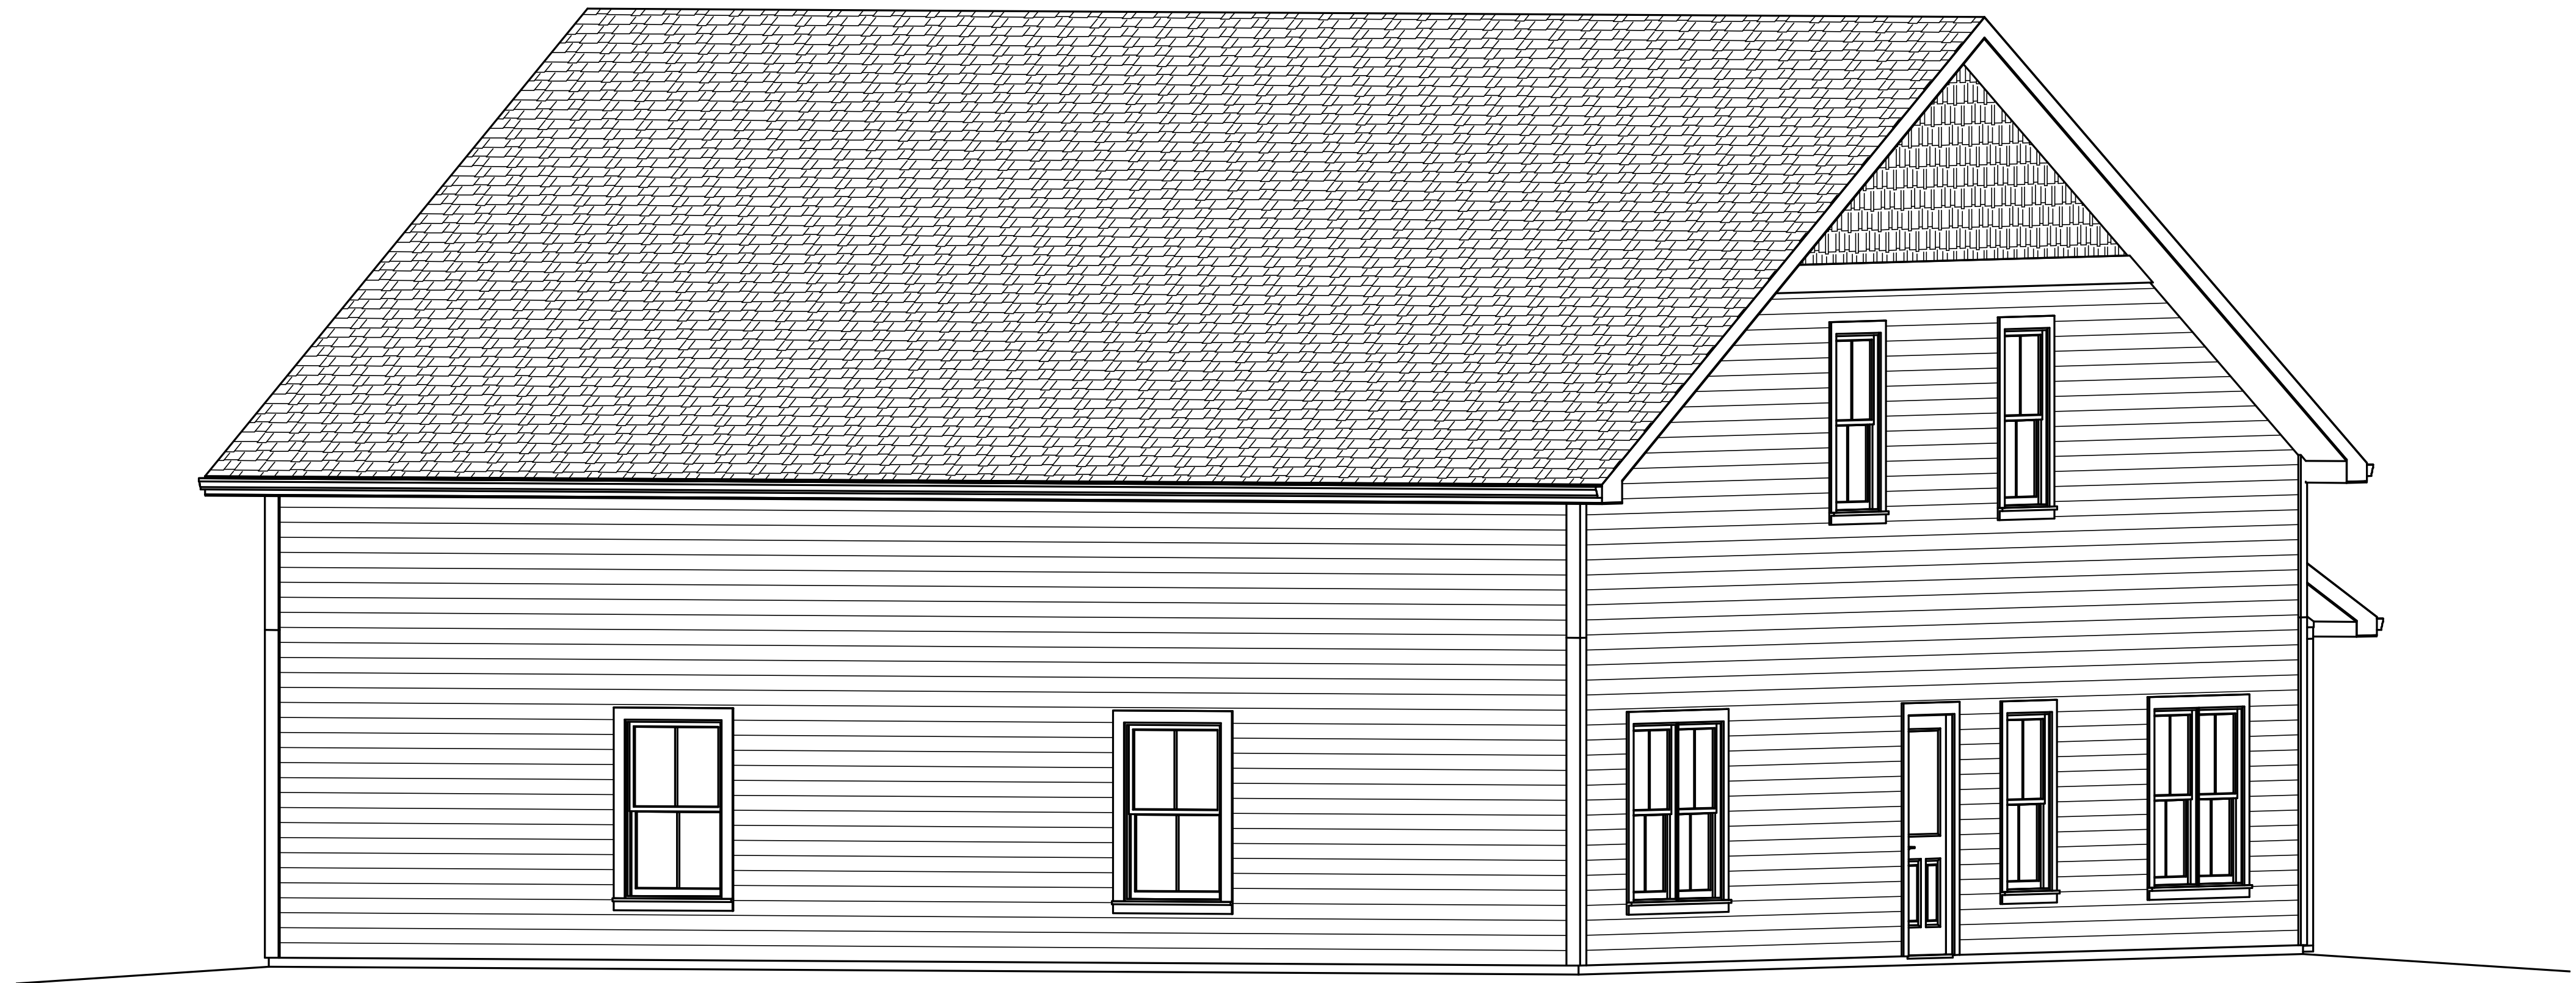

www.graberdrafting.com



SHEET SCHEDULE:

PAGE 2 MAIN & 2ND FLOOR PLANS

PAGE 3 FOUNDATION & ROOF PLANS

PAGE 4 ELEVATIONS



GRABER
DRAFTING
(812) 687-7653
www.graberdrafting.com

DRAWN BY :
FRED GRABER

START DATE
7/10/26


REVISED
7/13/26

DUPLEX PLANS FOR:
Kevin Spicer - 412 E Wylie Street C

PAGE


1 OF
4

GREAT CARE & EFFORT HAVE GONE INTO THE CREATION & THE DESIGN OF THESE PLANS. HOWEVER BECAUSE OF THE IMPOSSIBILITY OF PROVIDING DAY TO DAY "ON THE SITE" CONSULTATION, SUPERVISION AND CONTROL OVER THE ACTUAL CONSTRUCTION, GRABER DRAFTING ASSUMES NO RESPONSIBILITY FOR ANY DAMAGE, INCLUDING STRUCTURAL FAILURES, DUE TO ANY DEFICIENCIES, OMISSIONS, OR ERRORS IN THE DESIGN OF THESE PLANS. USERS OF THESE PLANS SHALL REVIEW THE PLANS AND CHECK ALL DIMENSIONS, QUANTITIES, SPACING, AND STRUCTURAL MEMBERS PRIOR TO BUILDING AND ORDERING MATERIALS. THE DESIGNER SHALL NOT BE HELD LIABLE FOR ERRORS.

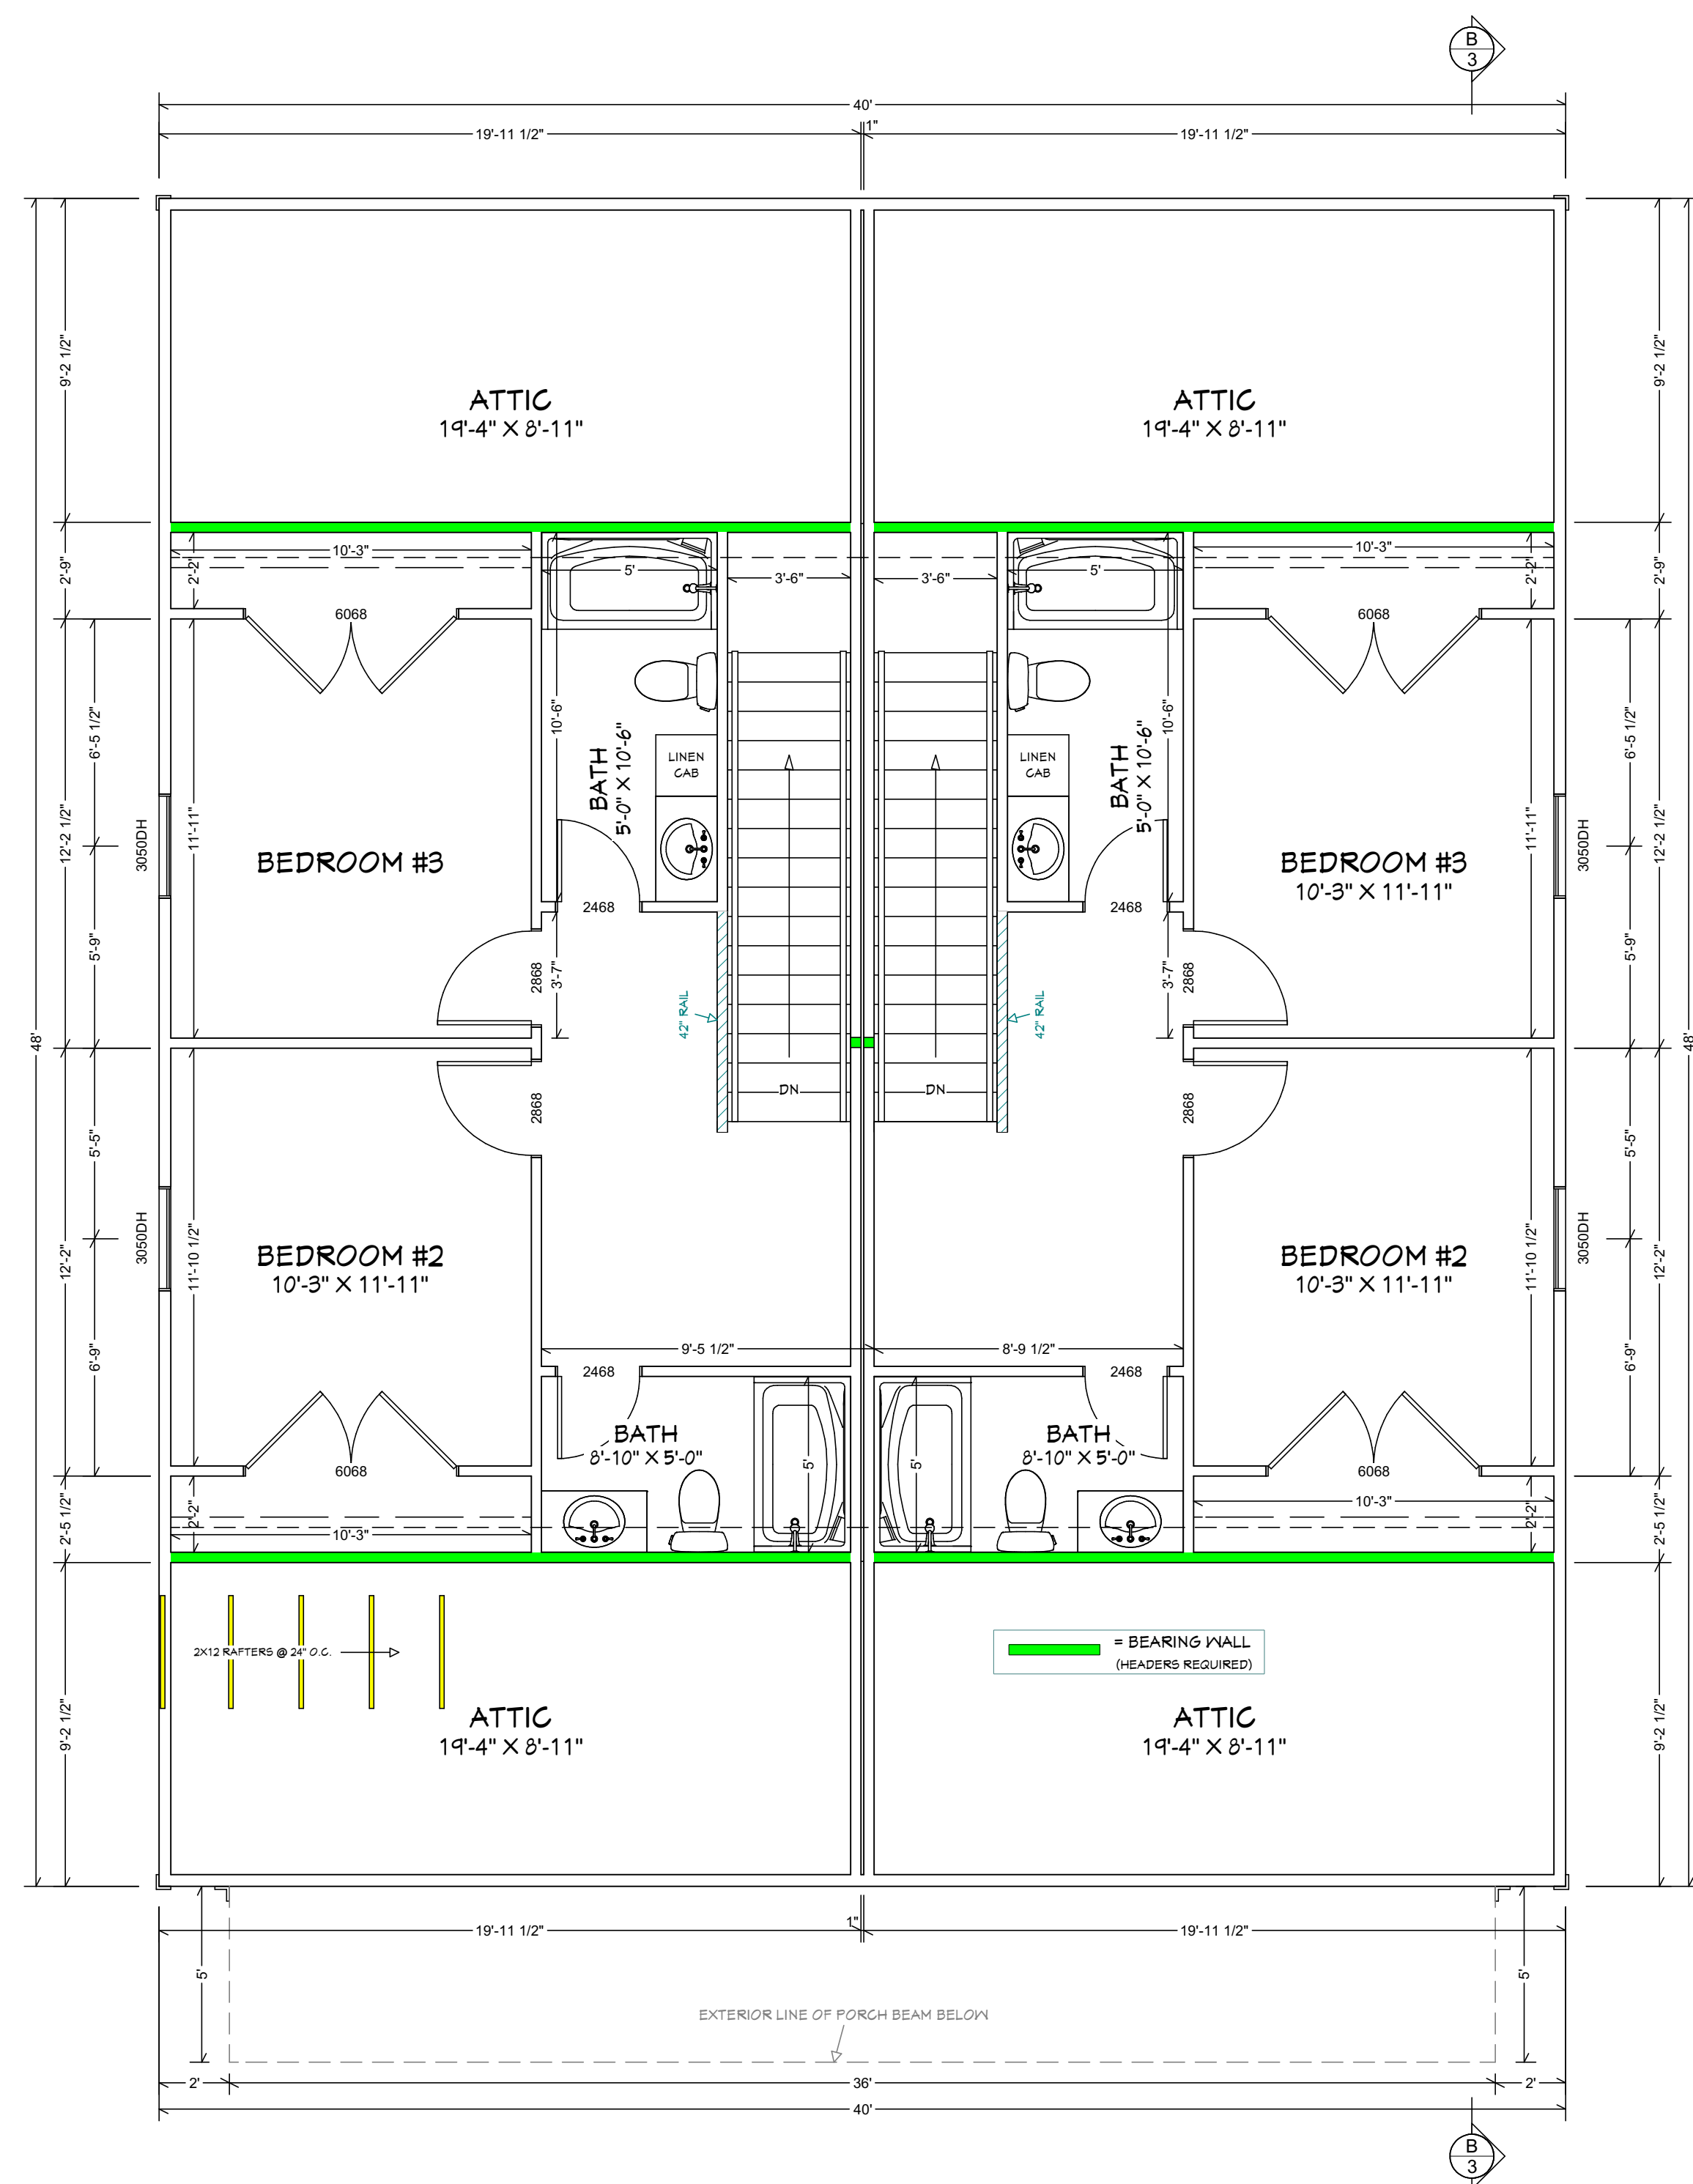

2ND FLOOR PLAN LIVING AREA 1076 SQ FT SCALE: 1/4" = 1'


WINDOW SCHEDULE					
LABEL	QTY	FLOOR	WIDTH	HEIGHT	DESCRIPTION
3050-2 DH	6	1	71 1/2"	59 1/2"	MULLED UNIT
3050DH	4	1	35 1/2"	59 1/2"	DOUBLE HUNG
3050DH	4	2	35 1/2"	59 1/2"	DOUBLE HUNG

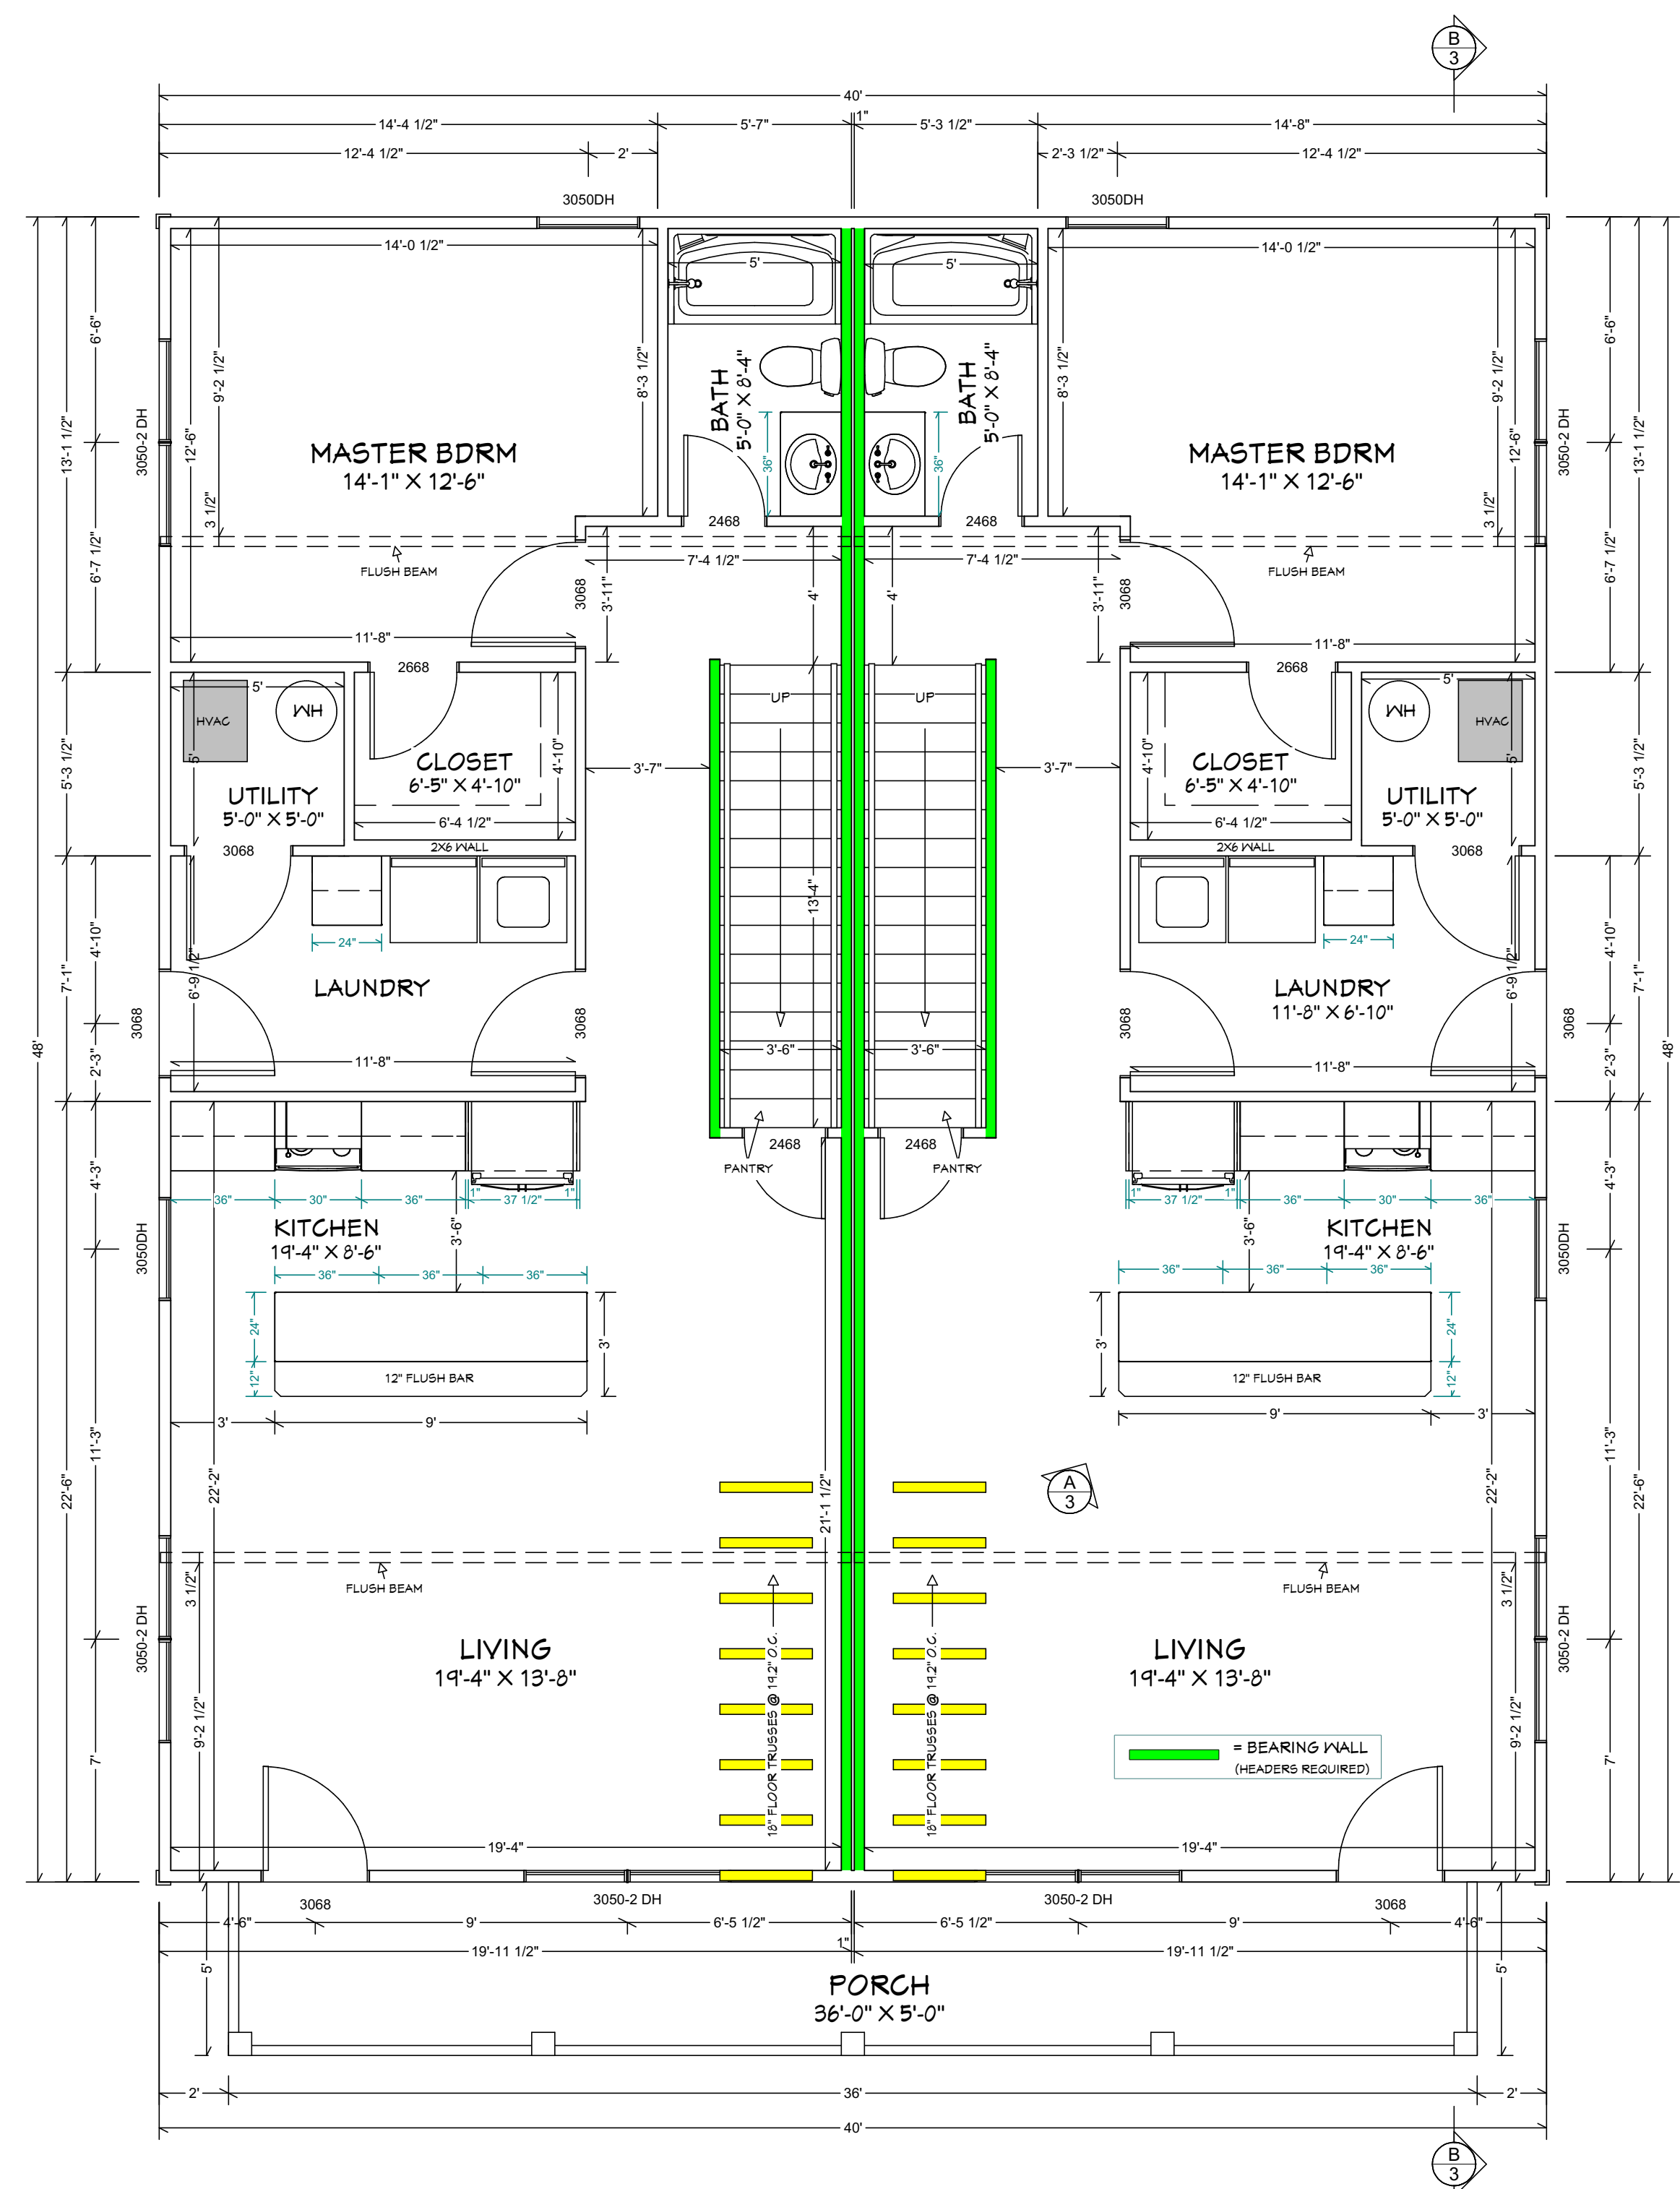

MAIN FLOOR PLAN LIVING AREA 1920 SQ FT SCALE: 1/4" = 1'

DOOR SCHEDULE						
LABEL	QTY	FLOOR	WIDTH	HEIGHT	DESCRIPTION	
2468	4	1	28"	80"	HINGED-DOOR	
2468	4	2	28"	80"	HINGED-DOOR	
2668	2	1	30"	80"	HINGED-DOOR	
2868	4	2	32"	80"	HINGED-DOOR	
3068	6	1	36"	80"	HINGED-DOOR	
3068	2	1	36"	80"	EXT. HINGED	
3068	2	1	36"	80"	EXT. HINGED-DOOR	
6068	4	2	72"	80"	DOUBLE HINGED-DOOR	

GREAT CARE & EFFORT HAVE GONE INTO THE CREATION & THE DESIGN OF THESE PLANS, HOWEVER BECAUSE OF THE IMPOSSIBILITY OF PROVIDING DAY TO DAY "ON THE SITE" CONSULTATION, SUPERVISION AND CONTROL OVER THE ACTUAL CONSTRUCTION, GRABER DRAFTING ASSUMES NO RESPONSIBILITY FOR ANY DAMAGE, INCLUDING STRUCTURAL FAILURES, DUE TO ANY DEFICIENCIES, OMISSIONS, OR ERRORS IN THE DESIGN OF THESE PLANS. USERS OF THESE PLANS SHALL REVIEW THE PLANS AND CHECK ALL DIMENSIONS, QUANTITIES, SPACING, AND STRUCTURAL MEMBERS PRIOR TO BUILDING AND ORDERING MATERIALS. THE DESIGNER SHALL NOT BE HELD LIABLE FOR ERRORS.

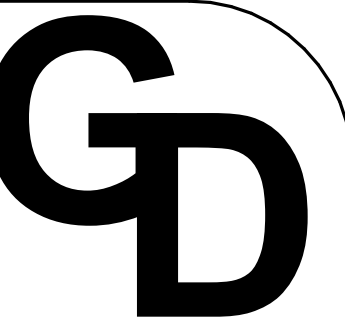

GRABER
DRAFTING
(812) 687-7653
www.graberdrafting.com

DRAWN BY :
FRED GRABER

START DATE
7/10/26

REVISED
7/13/26


DUPLEX PLANS FOR:
Kevin Spicer - 412 E Wylie Street C

PAGE

2 OF
4




A
3 3-D KITCHEN VIEW (NO SCALE)

 

ROOF PLAN
SCALE: 1/8" = 1'




B
3 **SCALE: 1/4" = 1'**

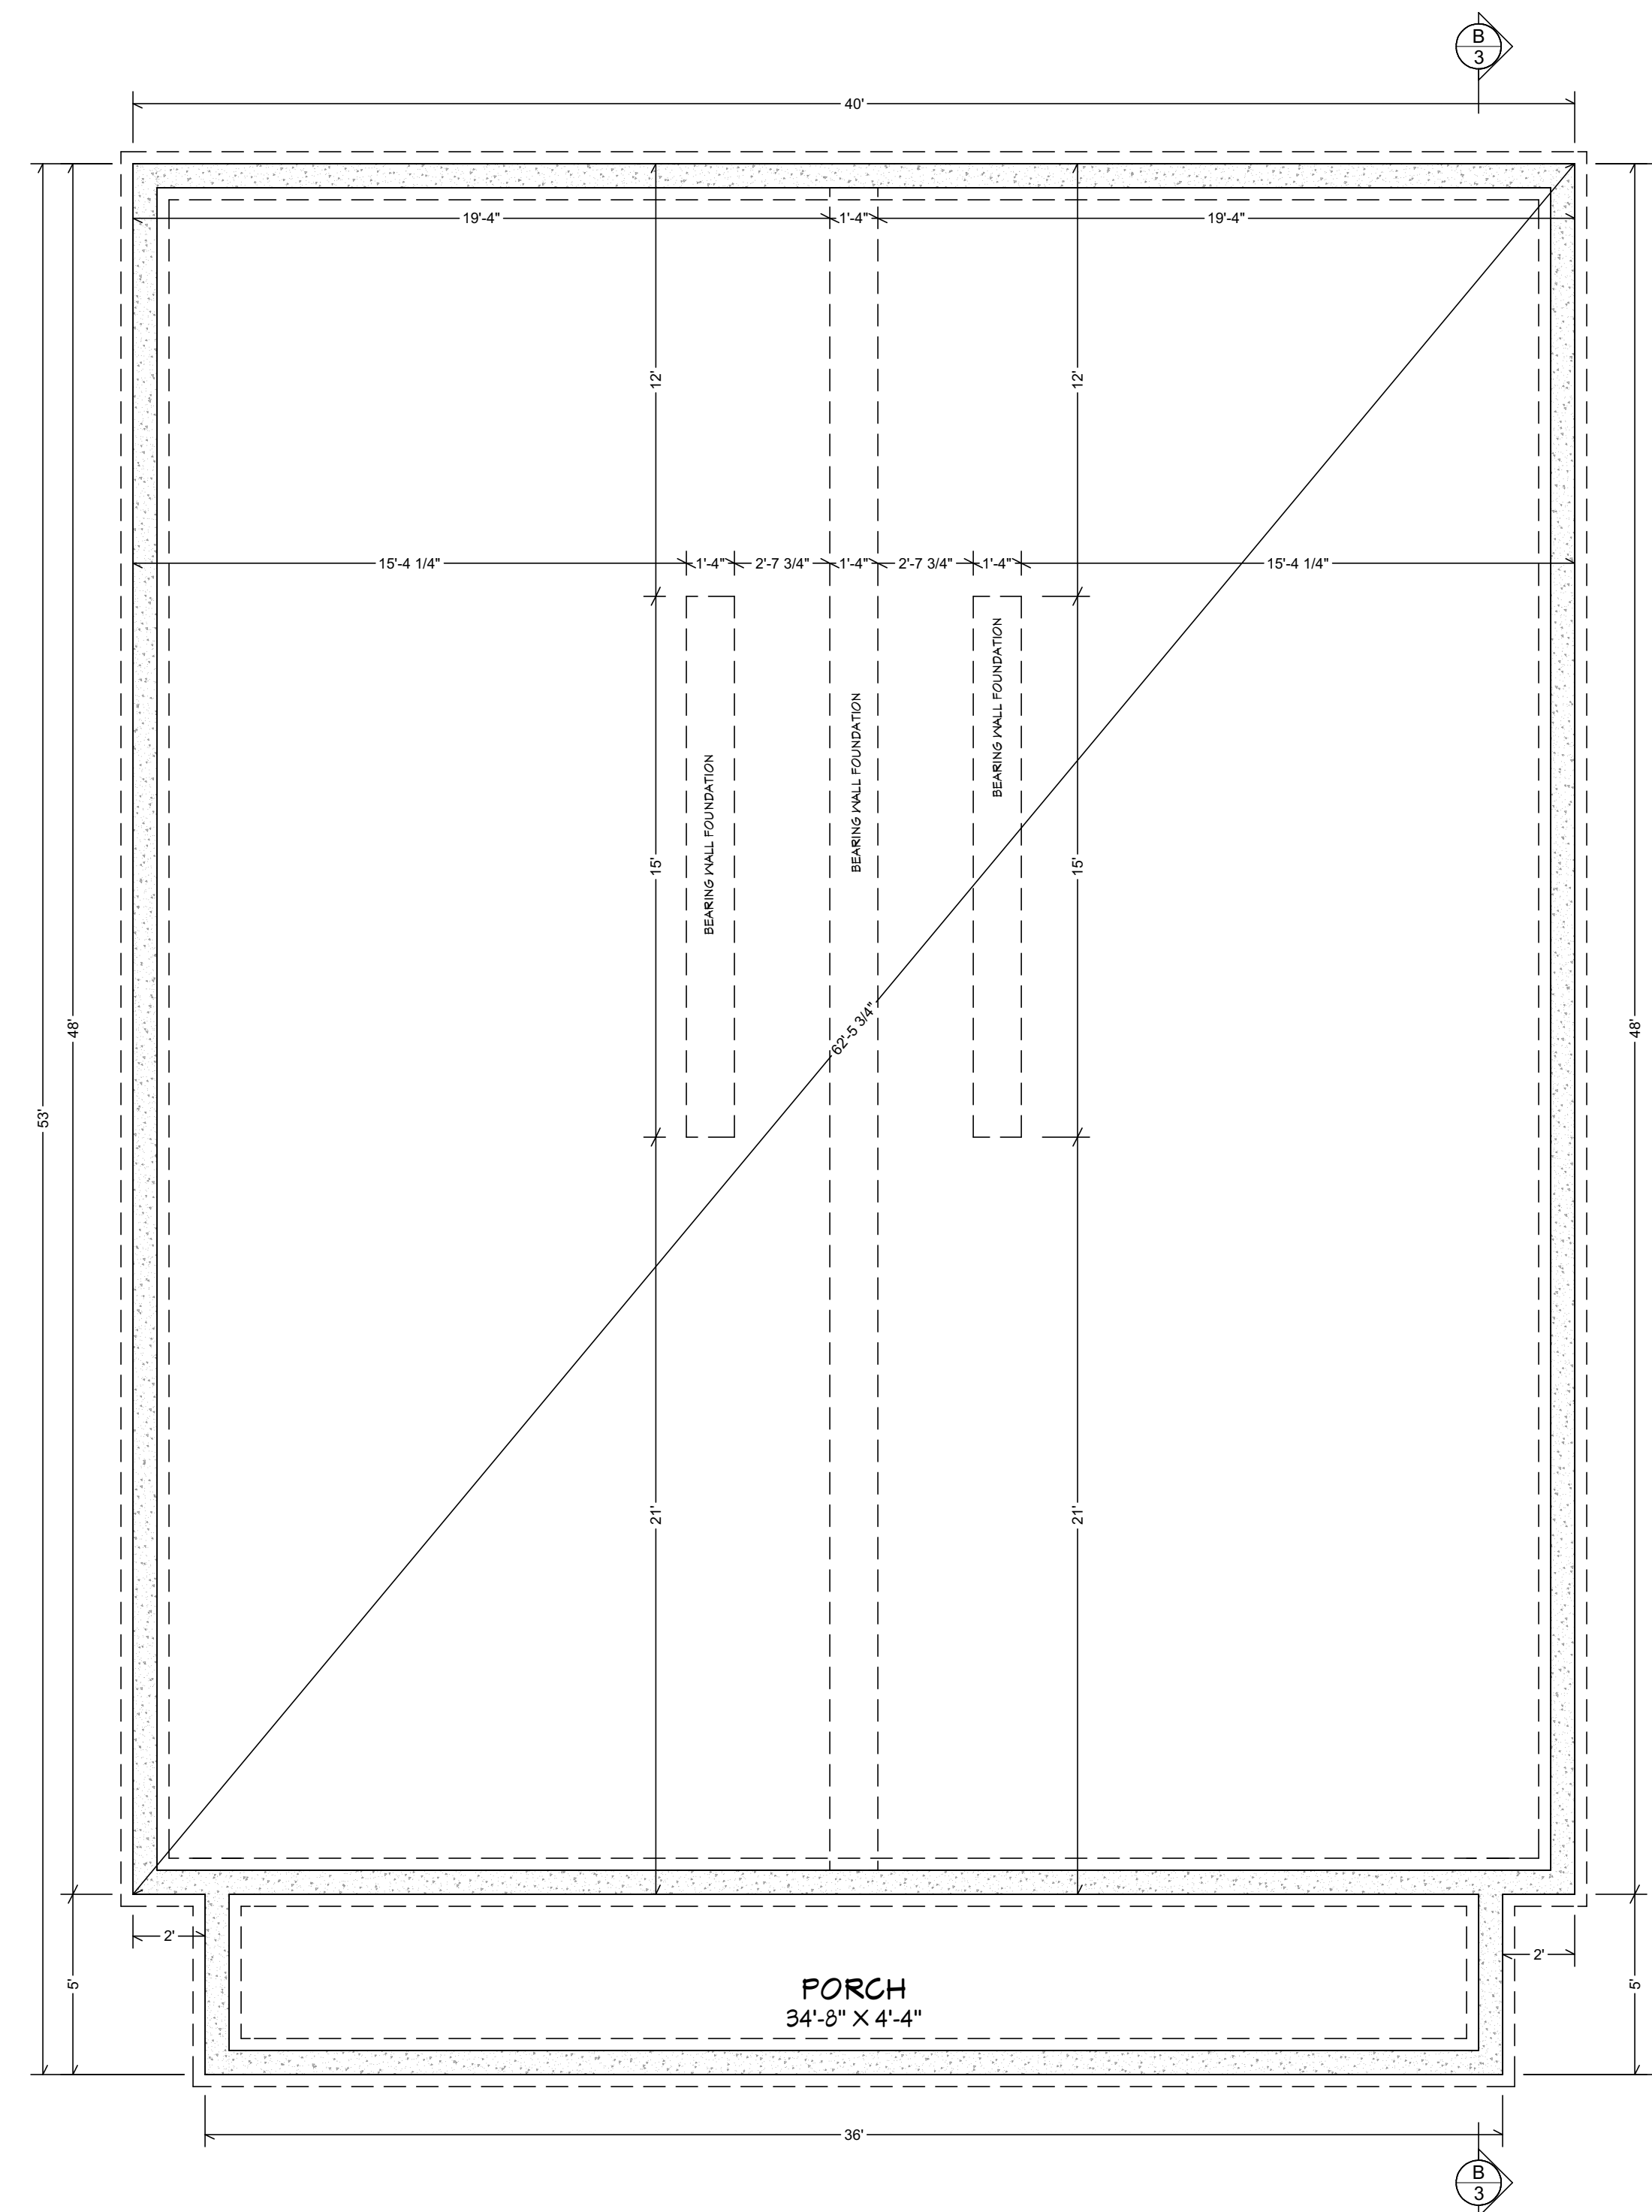

FOUNDATION PLAN

SCALE: 1/4" = 1'

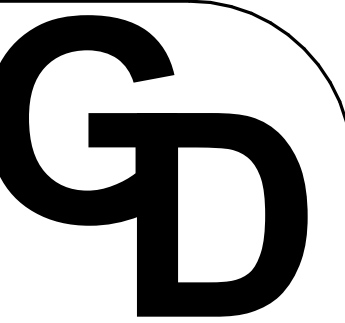

**GRABER
DRAFTING**
(812) 687-7653
www.graberdrafting.com

DRAWN BY :
FRED GRABER

START DATE
7/10/26


REVISED
7/13/26

DUPLEX PLANS FOR:
Kevin Spicer - 412 E Wylie Street C


PAGE

3 OF 4

GREAT CARE & EFFORT HAVE GONE INTO THE CREATION & THE DESIGN OF THESE PLANS, HOWEVER BECAUSE OF THE IMPOSSIBILITY OF PROVIDING DAY TO DAY "ON THE SITE" CONSULTATION, SUPERVISION AND CONTROL OVER THE ACTUAL CONSTRUCTION, GRABER DRAFTING ASSUMES NO RESPONSIBILITY FOR ANY DAMAGE, INCLUDING STRUCTURAL FAILURES, DUE TO ANY DEFICIENCIES, OMISSIONS, OR ERRORS IN THE DESIGN OF THESE PLANS. USERS OF THESE PLANS SHALL REVIEW THE PLANS AND CHECK ALL DIMENSIONS, QUANTITIES, SPACING, AND STRUCTURAL MEMBERS PRIOR TO BUILDING AND ORDERING MATERIALS. THE DESIGNER SHALL NOT BE HELD LIABLE FOR ERRORS.

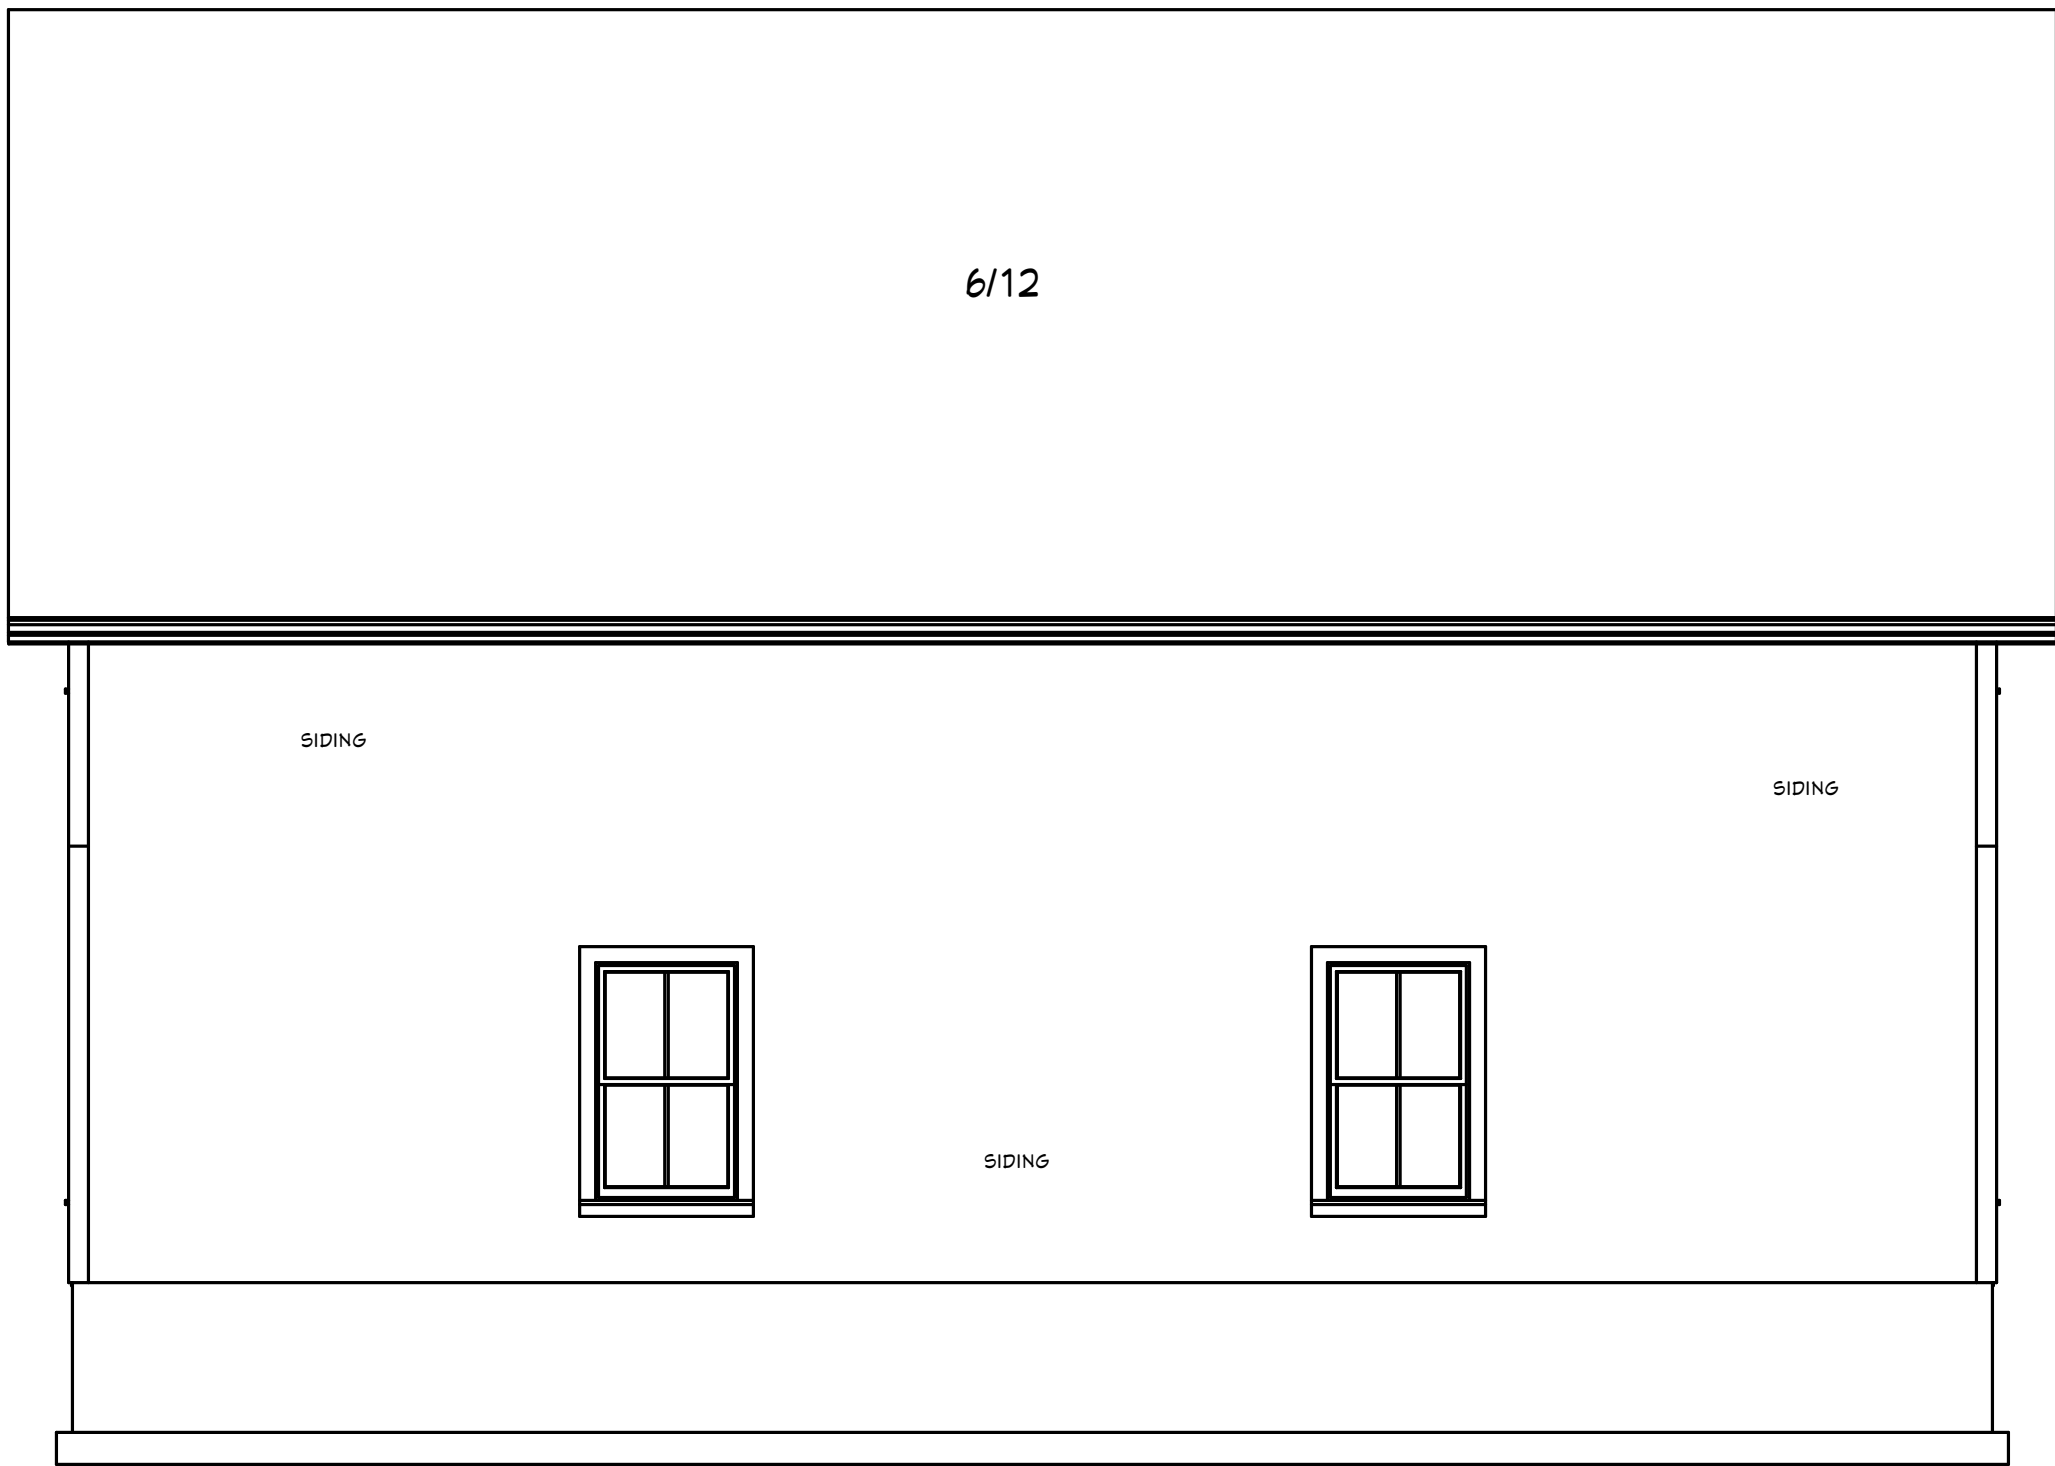

BACK ELEVATION
SCALE: 1/4" = 1'

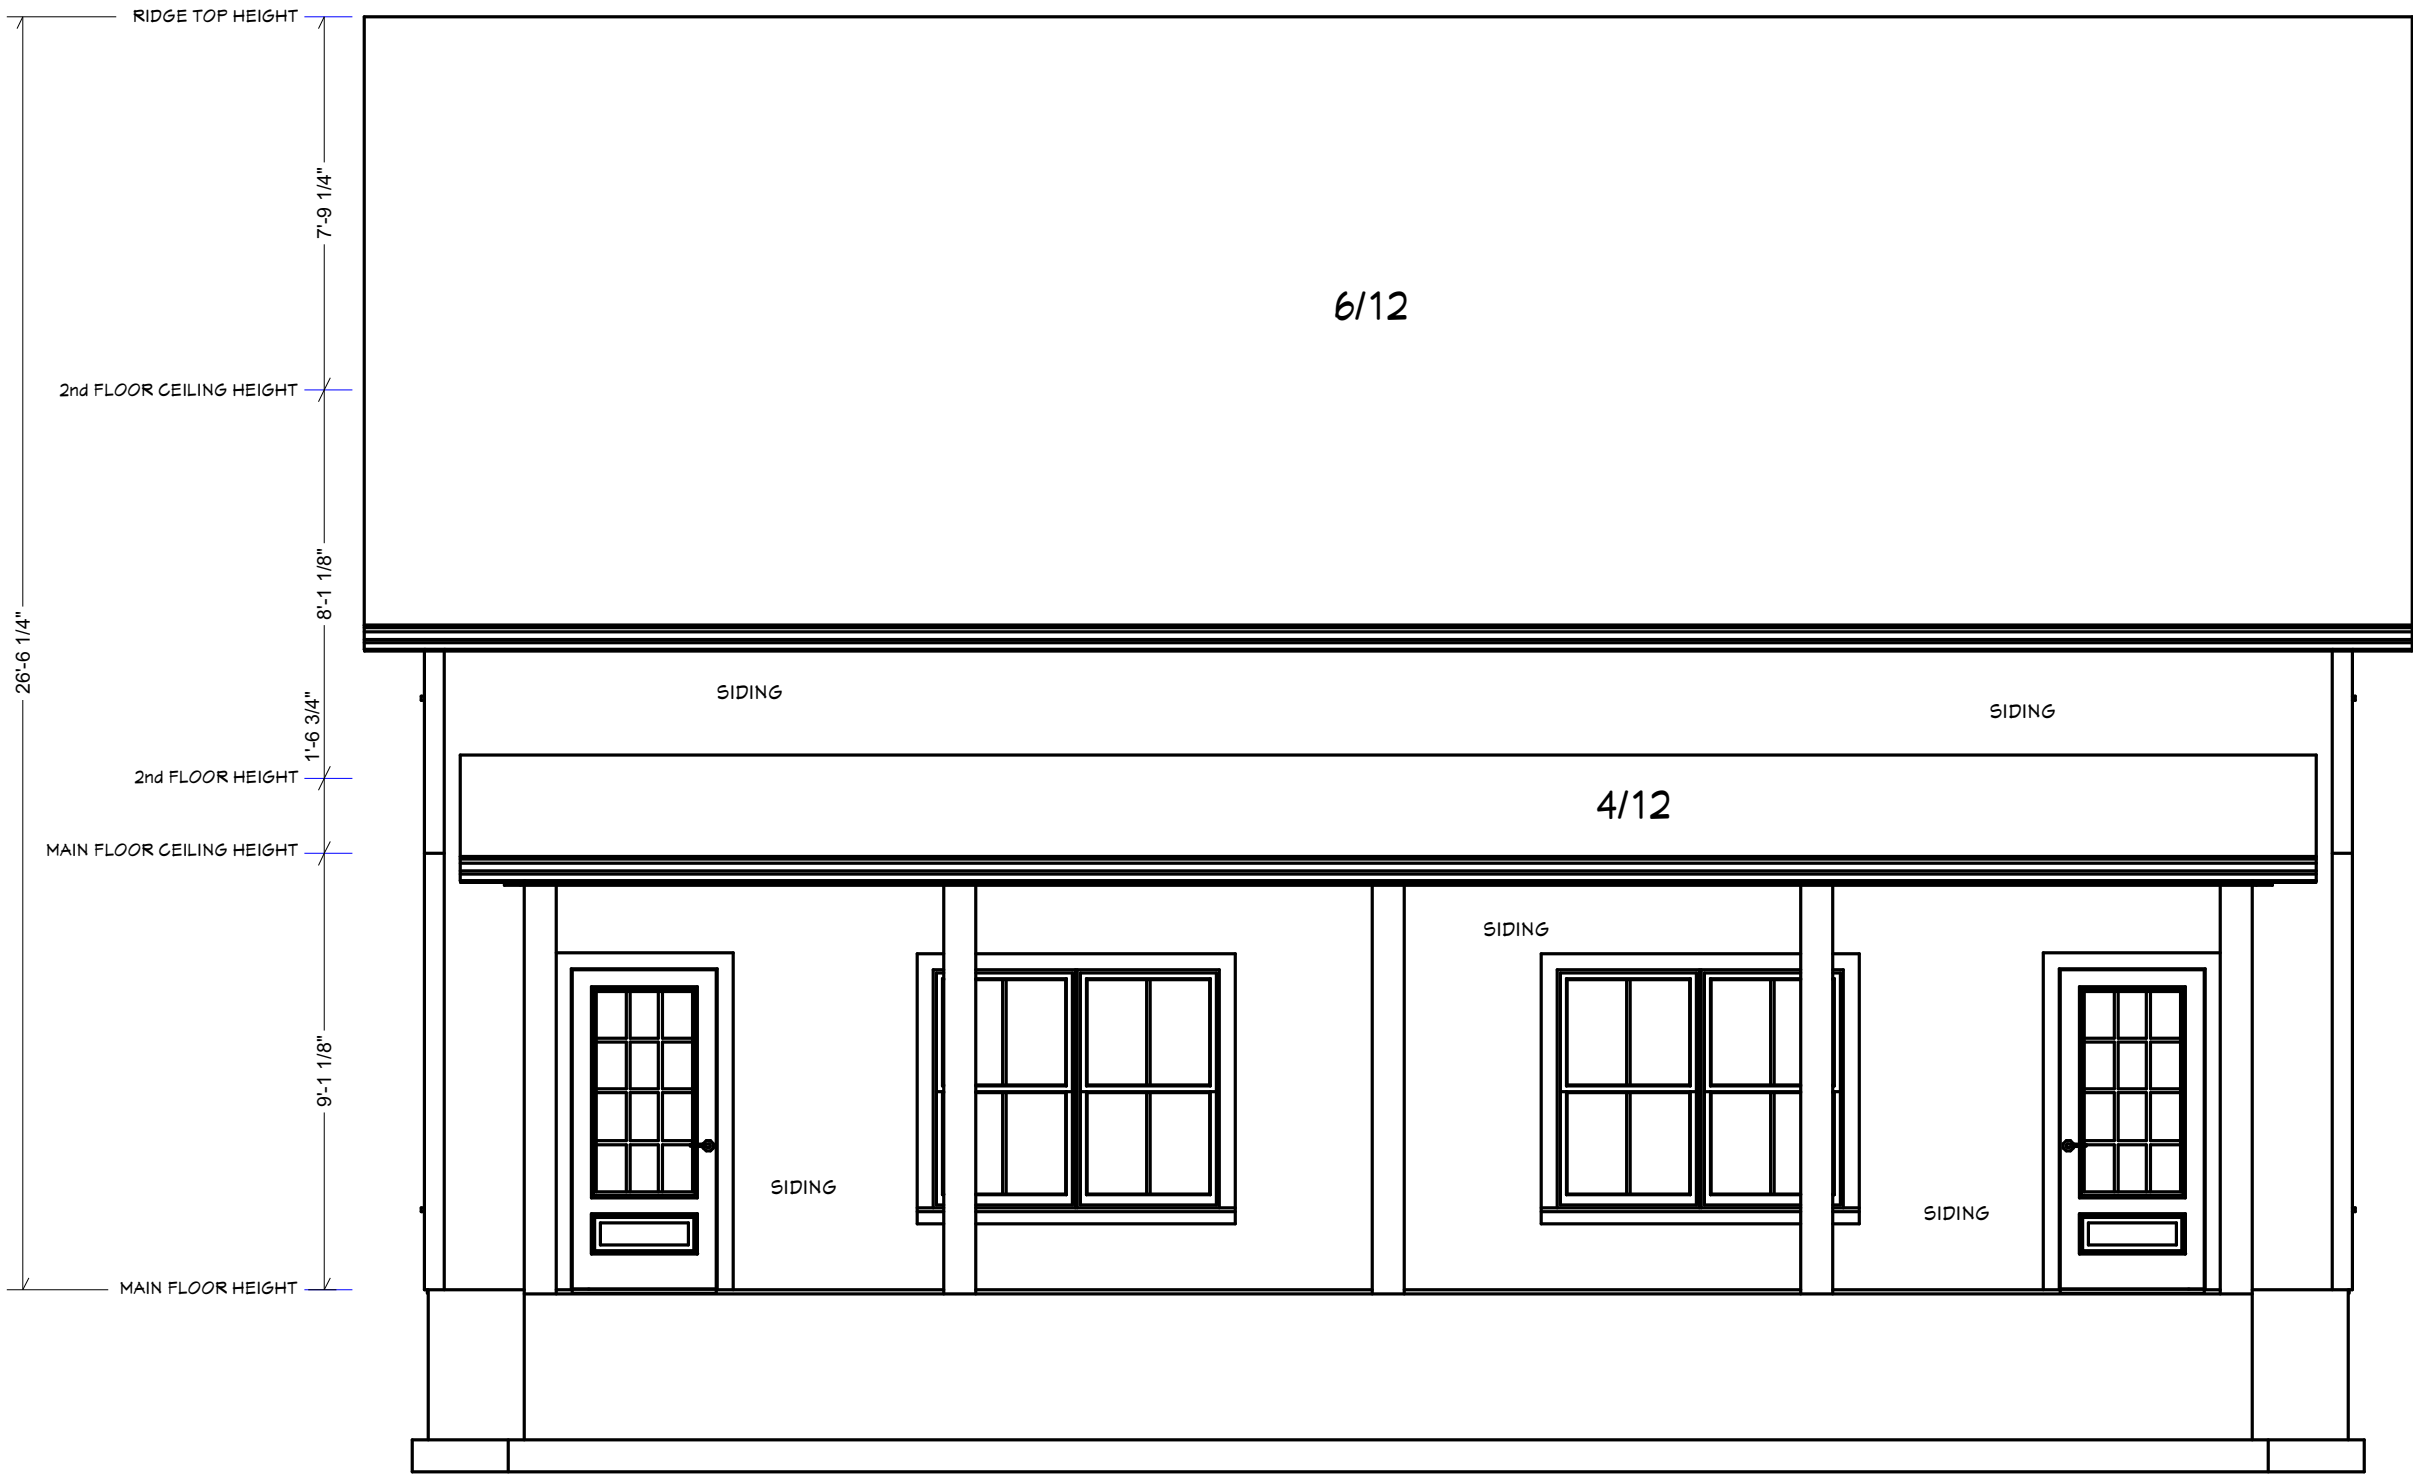

FRONT ELEVATION
SCALE: 1/4" = 1'



LEFT ELEVATION
SCALE: 1/4" = 1'



RIGHT ELEVATION
SCALE: 1/4" = 1'



GRABER
DRAFTING
(812) 687-7653
www.graberdrafting.com

DRAWN BY :
FRED GRABER

START DATE
7/10/26

REVISED
7/13/26

DUPLEX PLANS FOR:
Kevin Spicer - 412 E Wylie Street C

PAGE

4 OF
4

GREAT CARE & EFFORT HAVE GONE INTO THE CREATION & THE DESIGN OF THESE PLANS. HOWEVER BECAUSE OF THE IMPOSSIBILITY OF PROVIDING DAY TO DAY "ON THE SITE" CONSULTATION, SUPERVISION AND CONTROL OVER THE ACTUAL CONSTRUCTION, GRABER DRAFTING ASSUMES NO RESPONSIBILITY FOR ANY DAMAGE, INCLUDING STRUCTURAL FAILURES, DUE TO ANY DEFICIENCIES, OMISSIONS, OR ERRORS IN THE DESIGN OF THESE PLANS. USERS OF THESE PLANS SHALL REVIEW THE PLANS AND CHECK ALL DIMENSIONS, QUANTITIES, SPACING, AND STRUCTURAL MEMBERS PRIOR TO BUILDING AND ORDERING MATERIALS. THE DESIGNER SHALL NOT BE HELD LIABLE FOR ERRORS.